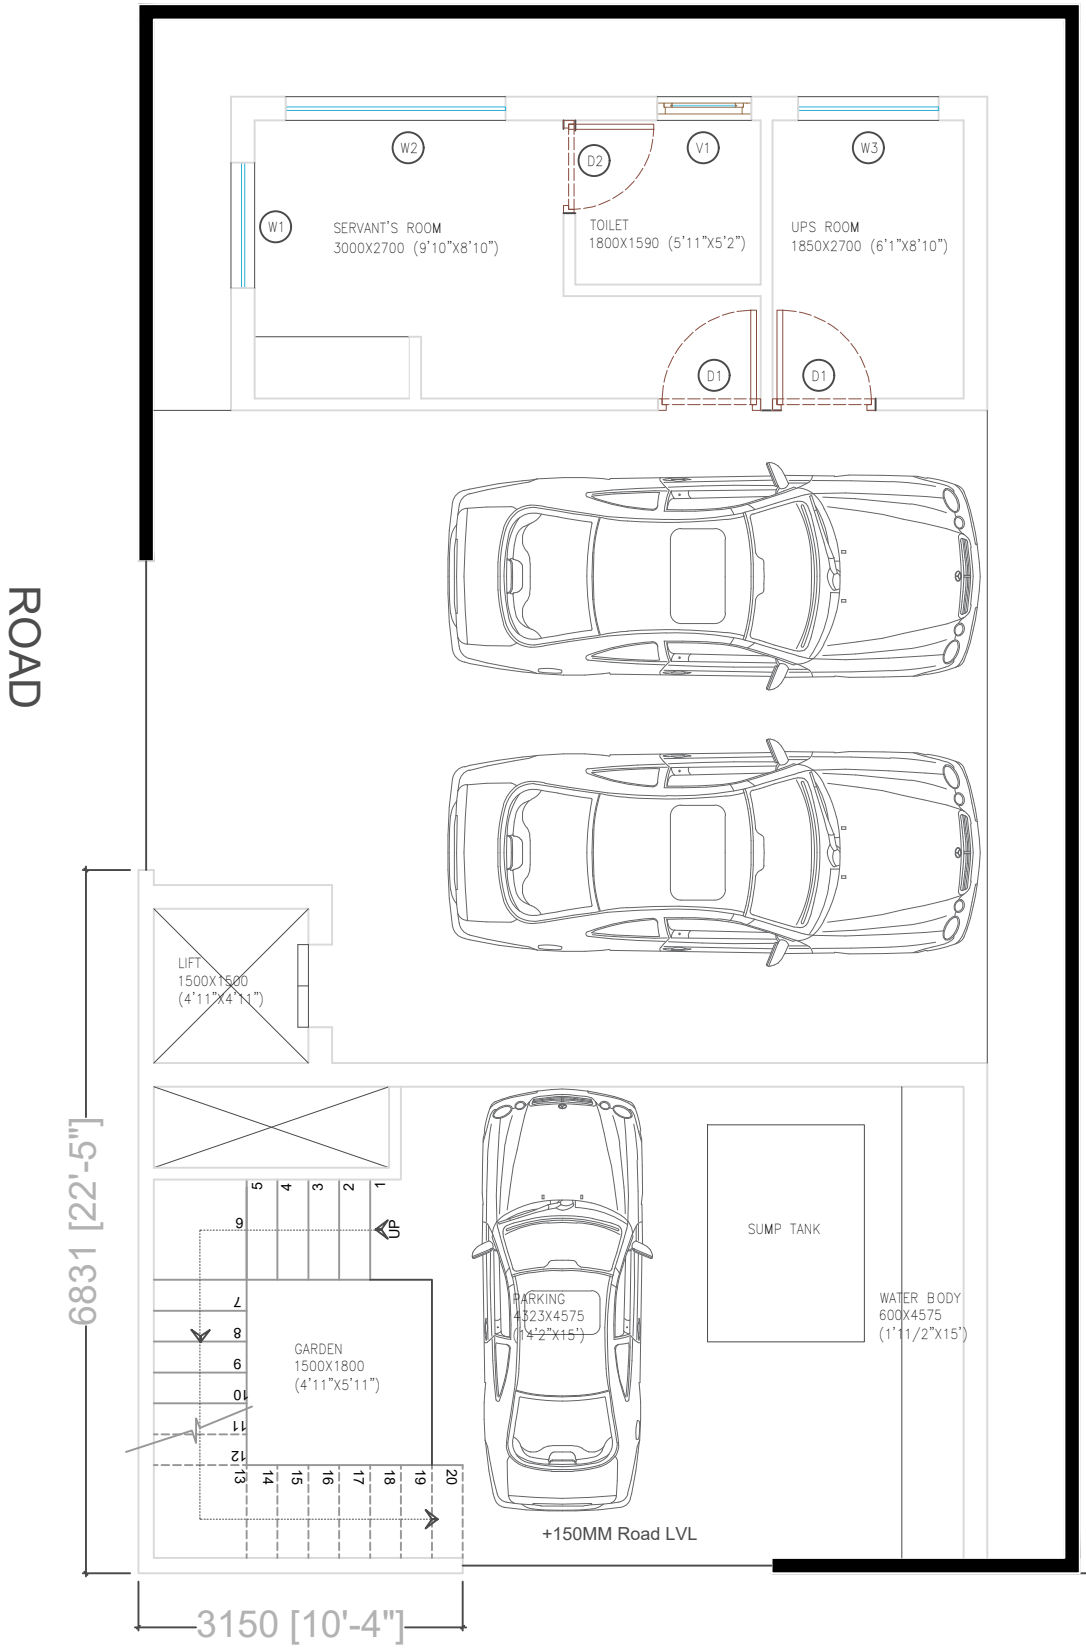

NOTES:

1. DO NOT SCALE THE DRAWING, FOLLOW ONLY FIGURED DIMENSIONS.
2. ALL DIMENSIONS GIVEN IN THIS DRAWING ARE IN FEET & INCHES UNLESS NOTED OTHERWISE.
3. ALL DIMENSIONS TO BE VERIFIED ON SITE AND APPROVED BY THE SITE ENGINEER.
4. ANY DISCREPANCY OR AMBIGUITY IN THE DRAWINGS SHOULD IMMEDIATELY BE BROUGHT TO NOTICE OF THE ARCHITECT.
5. ALL DRAWINGS SHOULD BE READ IN CONJUNCTION WITH OTHER RELEVANT ARCHITECTURAL, STRUCTURAL, PLUMBING, MECHANICAL AND ELECTRICAL DRAWINGS.
6. THE ± 0 REFERS TO LEVEL ESTABLISHED AT SITE IN PRESENCE OF THE SITE SUPERVISOR AND THE ARCHITECT.
ALL REMAINING LEVELS ARE RELATIVE TO THIS LEVEL.

GROUND FLOOR PLAN

Client:	
Purpose:	
Sheet Title:	GROUND FLOOR PLAN
Sheet No:	SH01
Design BY:	Prabhu Anandan
Contact:	
Scale:	NTS
Date:	15.06.2025

N

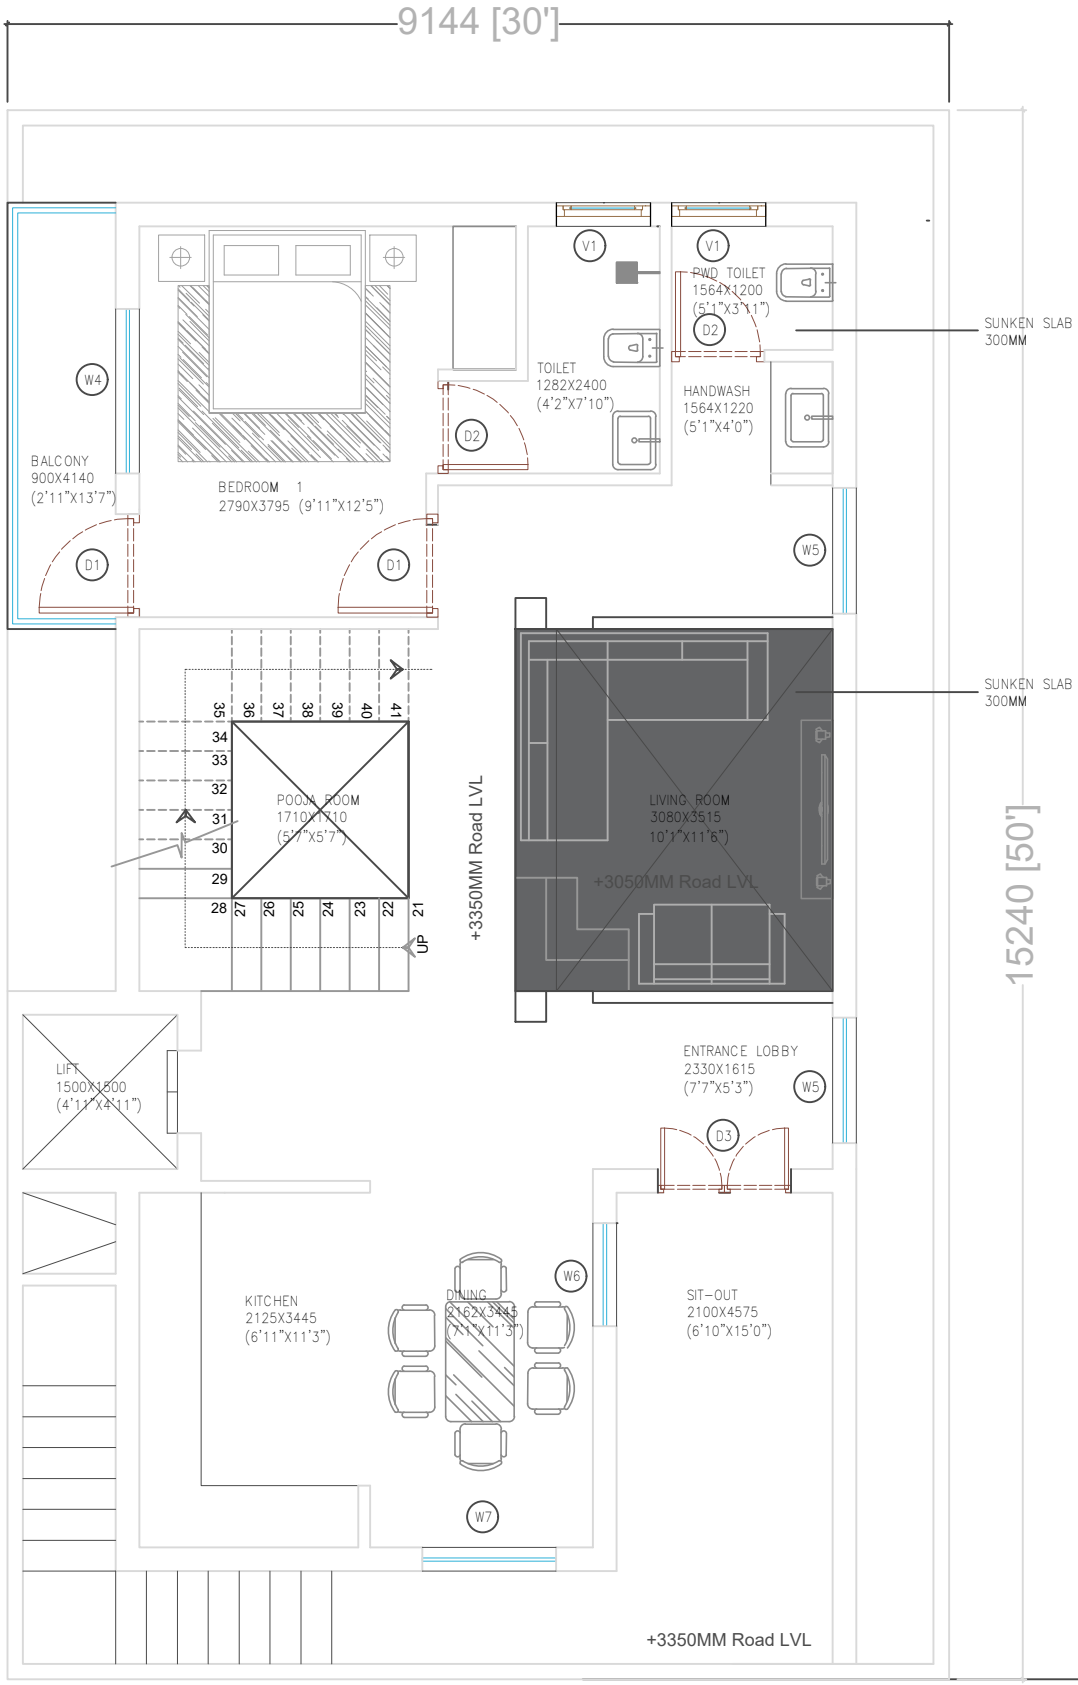

NOTES:

1. DO NOT SCALE THE DRAWING, FOLLOW ONLY FIGURED DIMENSIONS.
2. ALL DIMENSIONS GIVEN IN THIS DRAWING ARE IN FEET & INCHES UNLESS NOTED OTHERWISE.
3. ALL DIMENSIONS TO BE VERIFIED ON SITE AND APPROVED BY THE SITE ENGINEER.
4. ANY DISCREPANCY OR AMBIGUITY IN THE DRAWINGS SHOULD IMMEDIATELY BE BROUGHT TO NOTICE OF THE ARCHITECT.
5. ALL DRAWINGS SHOULD BE READ IN CONJUNCTION WITH OTHER RELEVANT ARCHITECTURAL, STRUCTURAL, PLUMBING, MECHANICAL AND ELECTRICAL DRAWINGS.
6. THE ± 0 REFERS TO LEVEL ESTABLISHED AT SITE IN PRESENCE OF THE SITE SUPERVISOR AND THE ARCHITECT.
   ALL REMAINING LEVELS ARE RELATIVE TO THIS LEVEL.

FIRST FLOOR PLAN

Client:	
Purpose:	
Sheet Title:	GROUND FLOOR PLAN
Sheet No:	SH02
Design By	Prabhu Anandan
Contact:	
Scale:	NTS
Date:	15.06.2025

N

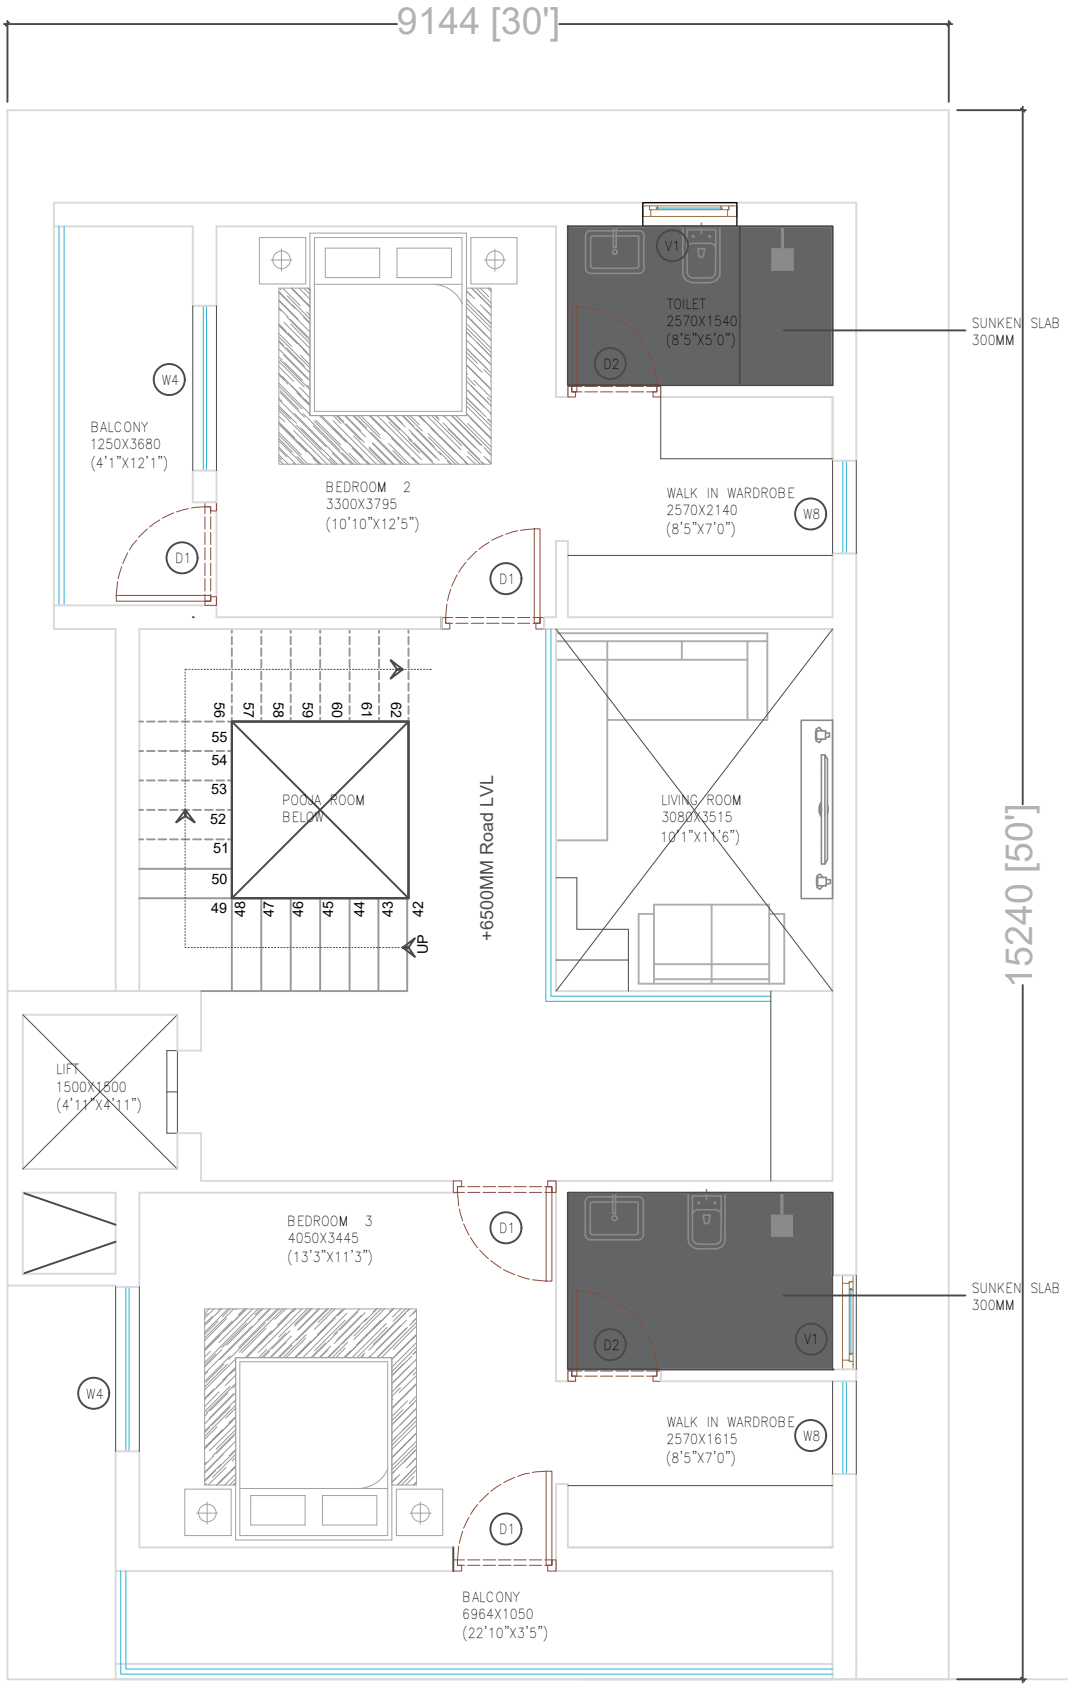

NOTES:

1. DO NOT SCALE THE DRAWING, FOLLOW ONLY FIGURED DIMENSIONS.
2. ALL DIMENSIONS GIVEN IN THIS DRAWING ARE IN FEET & INCHES UNLESS NOTED OTHERWISE.
3. ALL DIMENSIONS TO BE VERIFIED ON SITE AND APPROVED BY THE SITE ENGINEER.
4. ANY DISCREPANCY OR AMBIGUITY IN THE DRAWINGS SHOULD IMMEDIATELY BE BROUGHT TO NOTICE OF THE ARCHITECT.
5. ALL DRAWINGS SHOULD BE READ IN CONJUNCTION WITH OTHER RELEVANT ARCHITECTURAL, STRUCTURAL, PLUMBING, MECHANICAL AND ELECTRICAL DRAWINGS.
6. THE ± 0 REFERS TO LEVEL ESTABLISHED AT SITE IN PRESENCE OF THE SITE SUPERVISOR AND THE ARCHITECT.
   ALL REMAINING LEVELS ARE RELATIVE TO THIS LEVEL.

SECOND FLOOR PLAN

Client:	
Purpose:	
Sheet Title:	GROUND FLOOR PLAN
Sheet No:	SH03
Design By	Prabhu Anandan
Contact:	
Scale:	NTS
Date:	15.06.2025

N

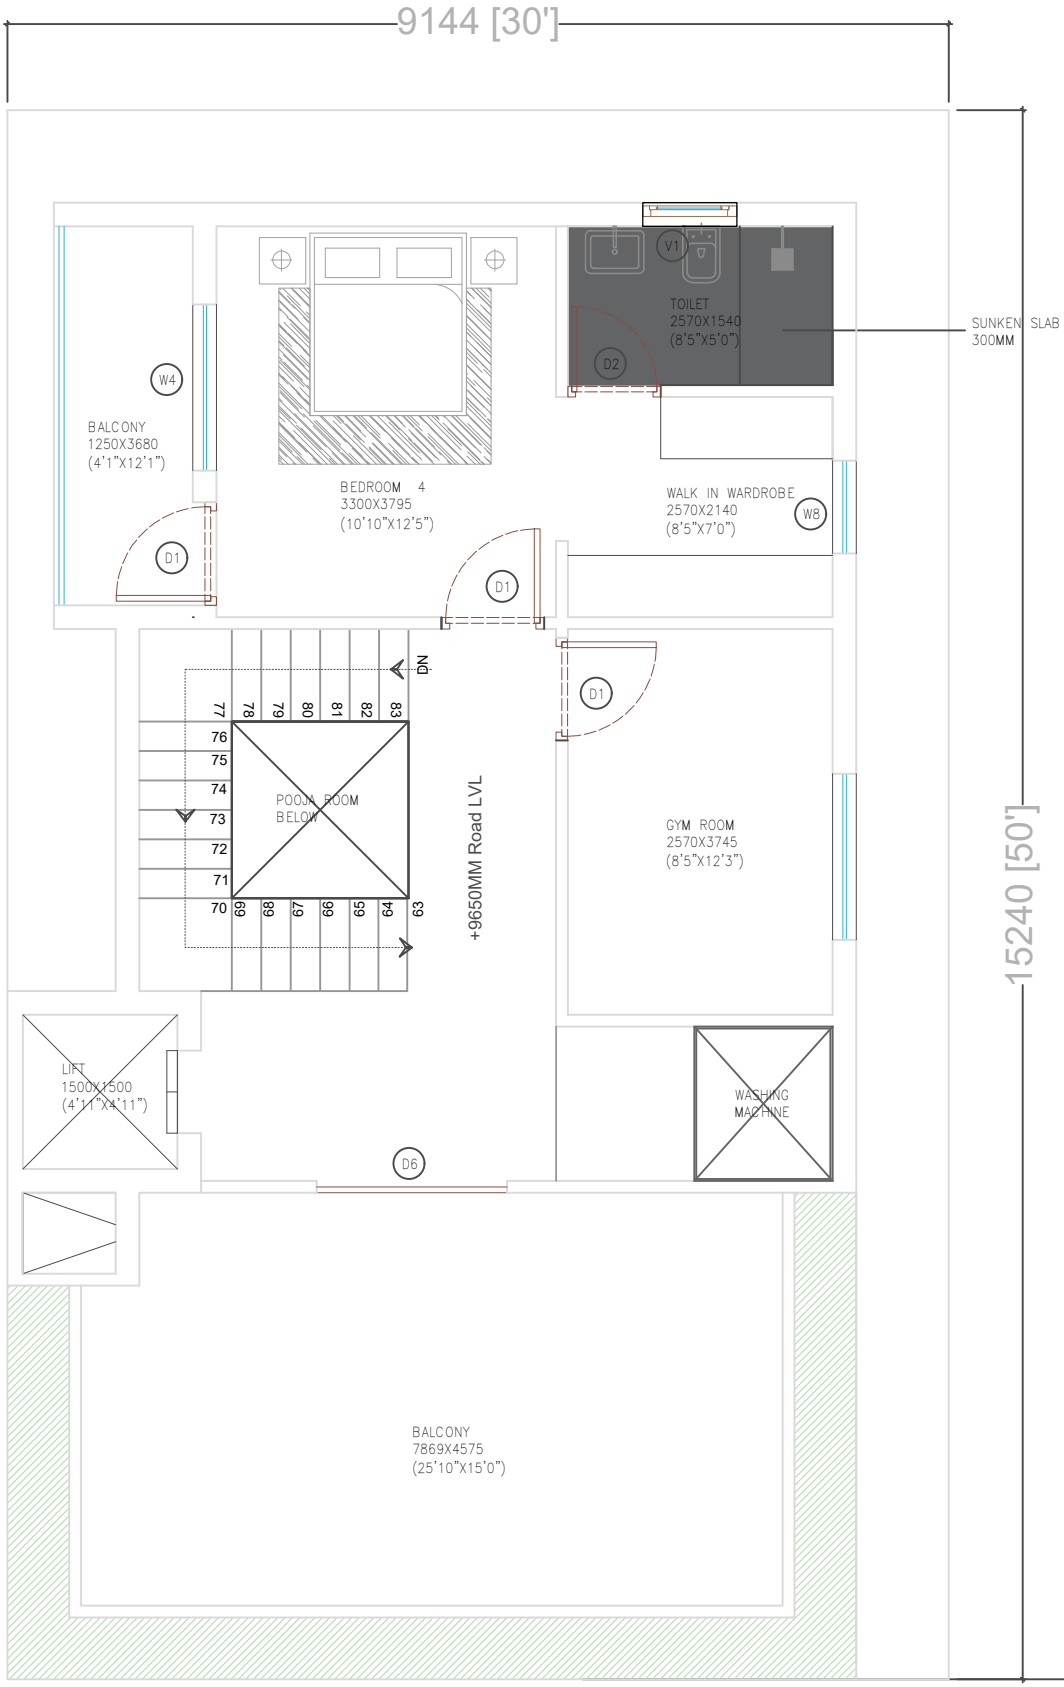

NOTES:

1. DO NOT SCALE THE DRAWING, FOLLOW ONLY FIGURED DIMENSIONS.
2. ALL DIMENSIONS GIVEN IN THIS DRAWING ARE IN MM UNLESS NOTED OTHERWISE.
3. ALL DIMENSIONS TO BE VERIFIED ON SITE AND APPROVED BY THE SITE ENGINEER.
4. ANY DISCREPANCY OR AMBIGUITY IN THE DRAWINGS SHOULD IMMEDIATELY BE BROUGHT TO NOTICE OF THE ARCHITECT.
5. ALL DRAWINGS SHOULD BE READ IN CONJUNCTION WITH OTHER RELEVANT ARCHITECTURAL, STRUCTURAL, PLUMBING, MECHANICAL AND ELECTRICAL DRAWINGS.
6. THE ± 0 REFERS TO LEVEL ESTABLISHED AT SITE IN PRESENCE OF THE SITE SUPERVISOR AND THE ARCHITECT.
   ALL REMAINING LEVELS ARE RELATIVE TO THIS LEVEL.

THIRD FLOOR PLAN

Client:	
Purpose:	
Sheet Title:	GROUND FLOOR PLAN
Sheet No:	SH01
Design By	Prabhu Anandan
Contact:	
Scale:	NTS
Date:	15.06.2025

N

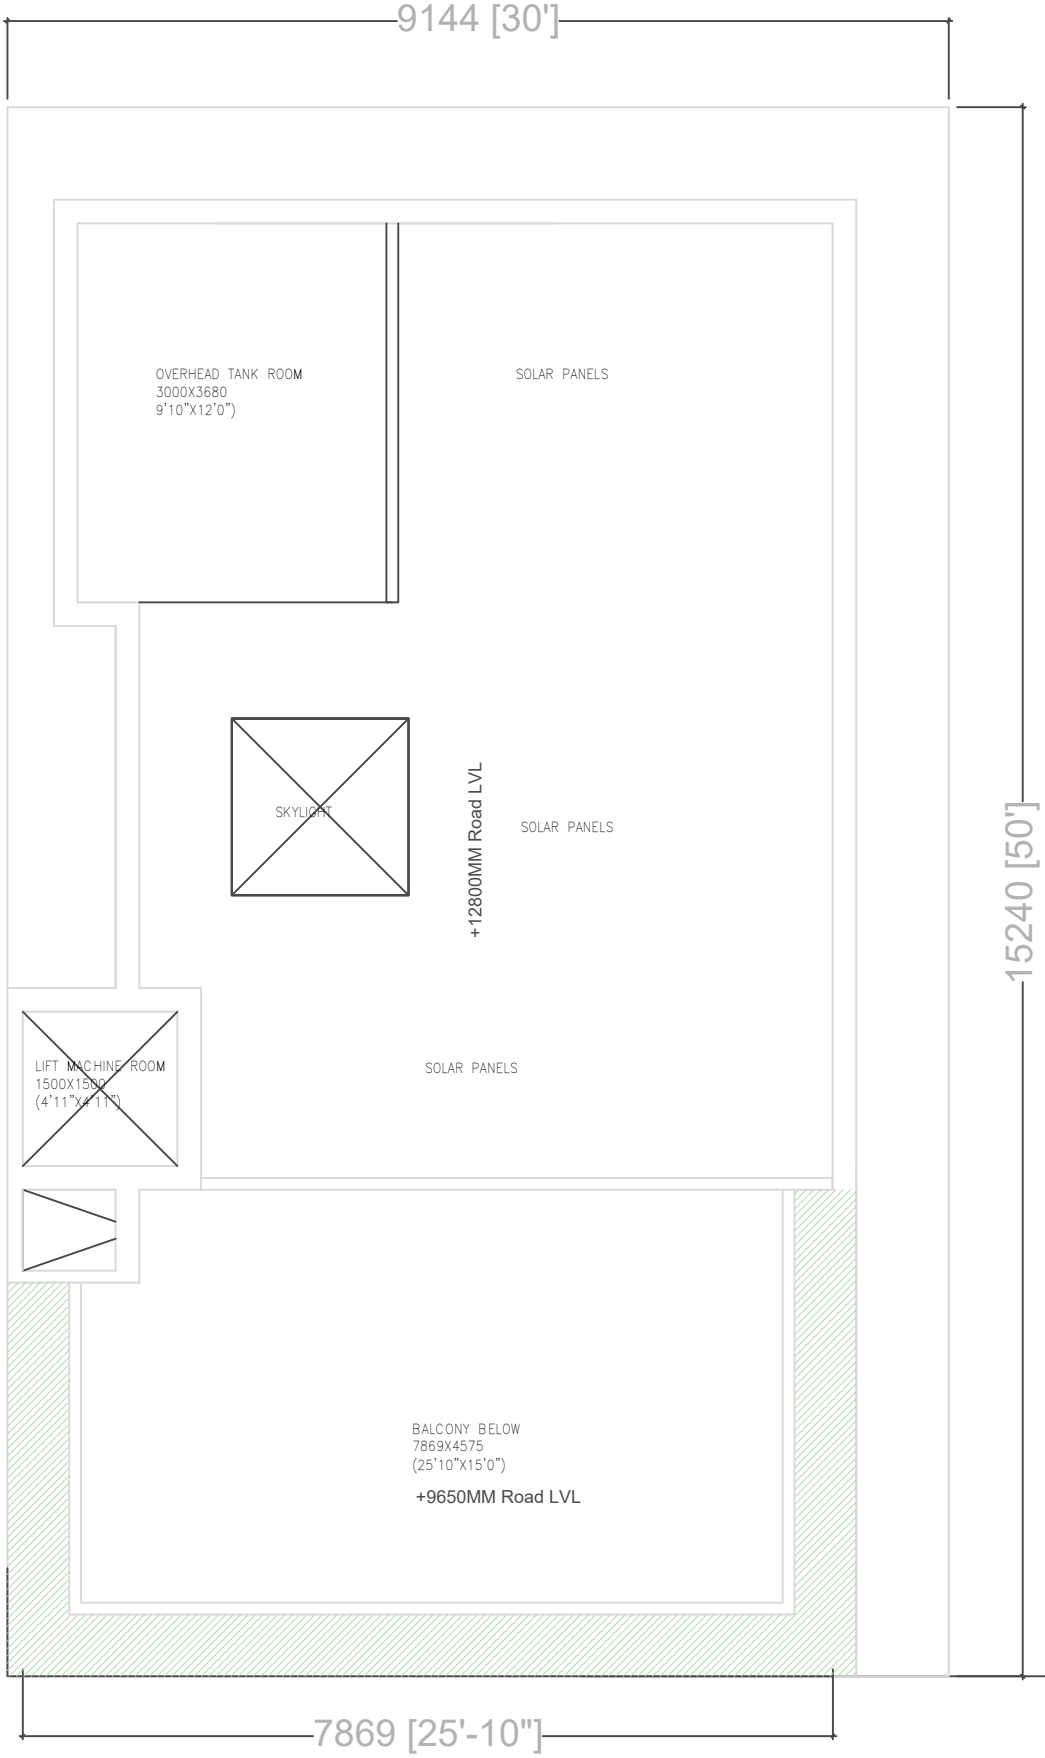

NOTES:

1. DO NOT SCALE THE DRAWING, FOLLOW ONLY FIGURED DIMENSIONS.
2. ALL DIMENSIONS GIVEN IN THIS DRAWING ARE IN FEET & INCHES UNLESS NOTED OTHERWISE.
3. ALL DIMENSIONS TO BE VERIFIED ON SITE AND APPROVED BY THE SITE ENGINEER.
4. ANY DISCREPANCY OR AMBIGUITY IN THE DRAWINGS SHOULD IMMEDIATELY BE BROUGHT TO NOTICE OF THE ARCHITECT.
5. ALL DRAWINGS SHOULD BE READ IN CONJUNCTION WITH OTHER RELEVANT ARCHITECTURAL, STRUCTURAL, PLUMBING, MECHANICAL AND ELECTRICAL DRAWINGS.
6. THE ± 0 REFERS TO LEVEL ESTABLISHED AT SITE IN PRESENCE OF THE SITE SUPERVISOR AND THE ARCHITECT.
ALL REMAINING LEVELS ARE RELATIVE TO THIS LEVEL.

TERRACE FLOOR PLAN

Client:	
Purpose:	
Sheet Title:	GROUND FLOOR PLAN
Sheet No:	SH01
Design By	AR.NIHARIKA
Contact:	
Scale:	NTS
Date:	15.06.2025

N

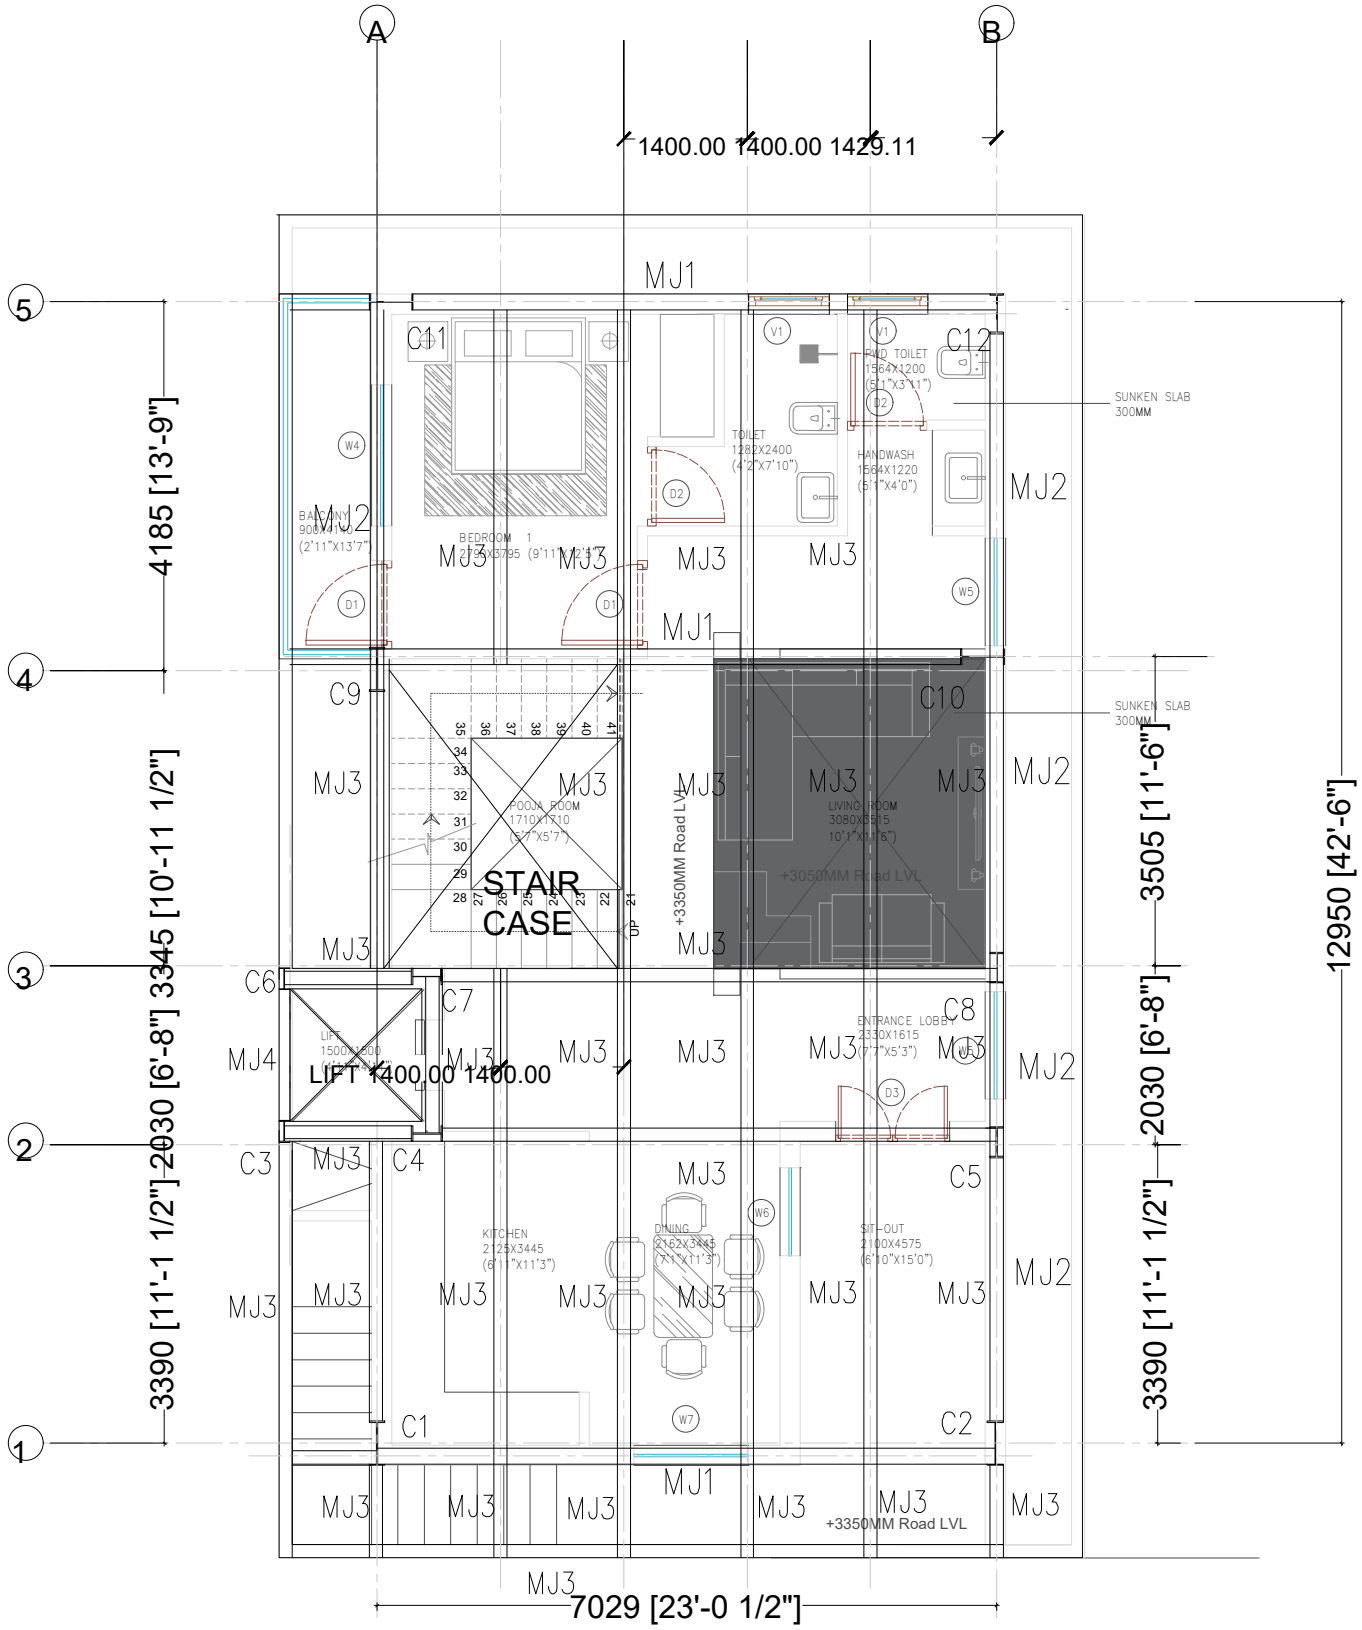
A
B
1400.00 1400.00 1429.11
5
4
3
2
1
4185 [13'-9"]
3345 [10'-11 1/2"]
2030 [6'-8"]
3390 [11'-1 1/2"]
3505 [11'-6"]
2030 [6'-8"]
3390 [11'-1 1/2"]
12950 [42'-6"]
7029 [23'-0 1/2"]
MJ1
MJ2
MJ3
MJ4
C1
C2
C3
C4
C5
C6
C7
C8
C9
C10
C11
C12
BALCONY
BEDROOM 1
TOILET
HANDWASH
SUNKEN SLAB 300MM
POOJA ROOM
STAIR CASE
+3350MM Road LVL
LIVING ROOM
+3050MM Road LVL
LIFT
LIFT 1400.00 1400.00
ENTRANCE LOBBY
KITCHEN
DINING
SIT-OUT
+3350MM Road LVL

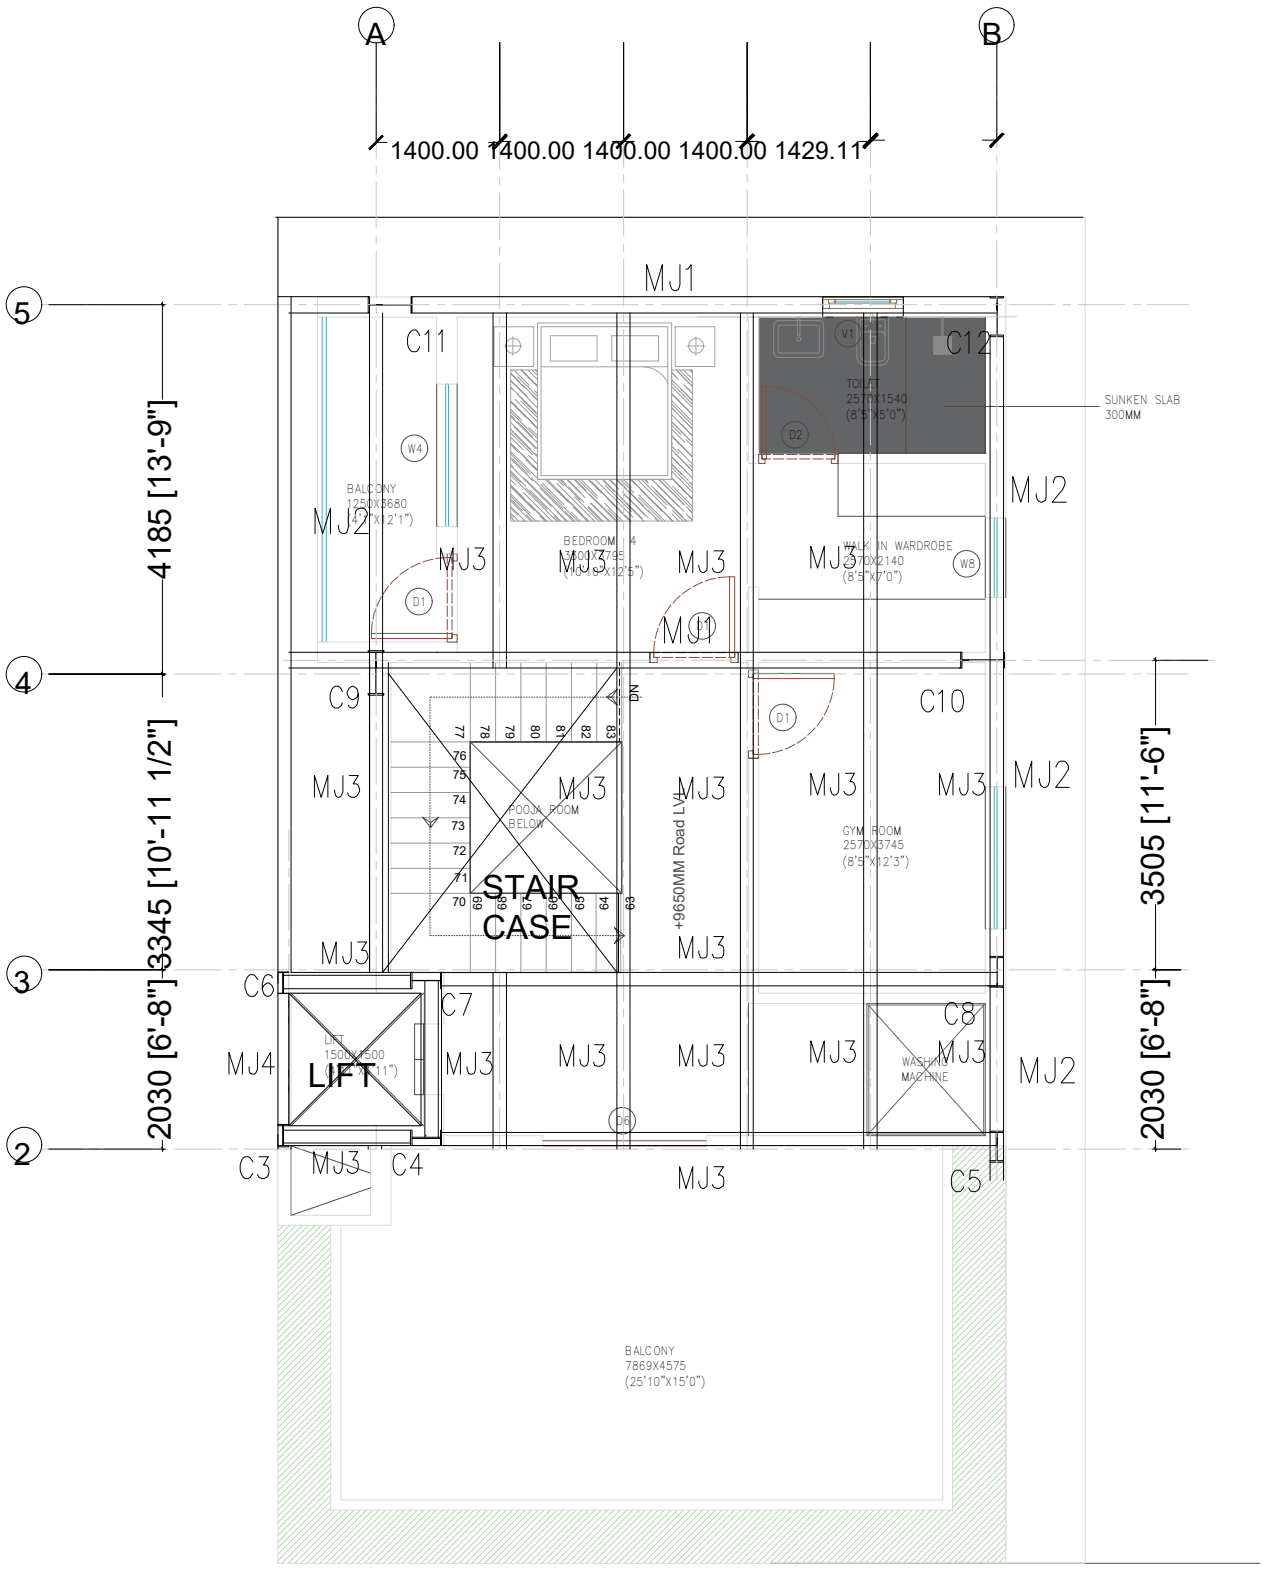
A
B
1400.00 1400.00 1400.00 1400.00 1429.11
5
4
3
2
4185 [13'-9"]
3345 [10'-11 1/2"]
2030 [6'-8"]
3505 [11'-6"]
2030 [6'-8"]
MJ1
MJ2
MJ3
MJ4
C11
C12
C9
C10
C6
C7
C8
C3
C4
C5
W4
D1
D2
V1
W8
BALCONY
1250X3680
(4'1"X12'1")
BEDROOM 4
3400X3795
(11'-3"X12'5")
TOILET
2570X1540
(8'5"X5'0")
SUNKEN SLAB
300MM
WALK IN WARDROBE
2570X2140
(8'5"X7'0")
POOJA ROOM
BELOW
STAIR
CASE
DN
+9650MM Road LVL
GYM ROOM
2570X3745
(8'5"X12'3")
LIFT
WASHING
MACHINE
BALCONY
7869X4575
(25'10"X15'0")

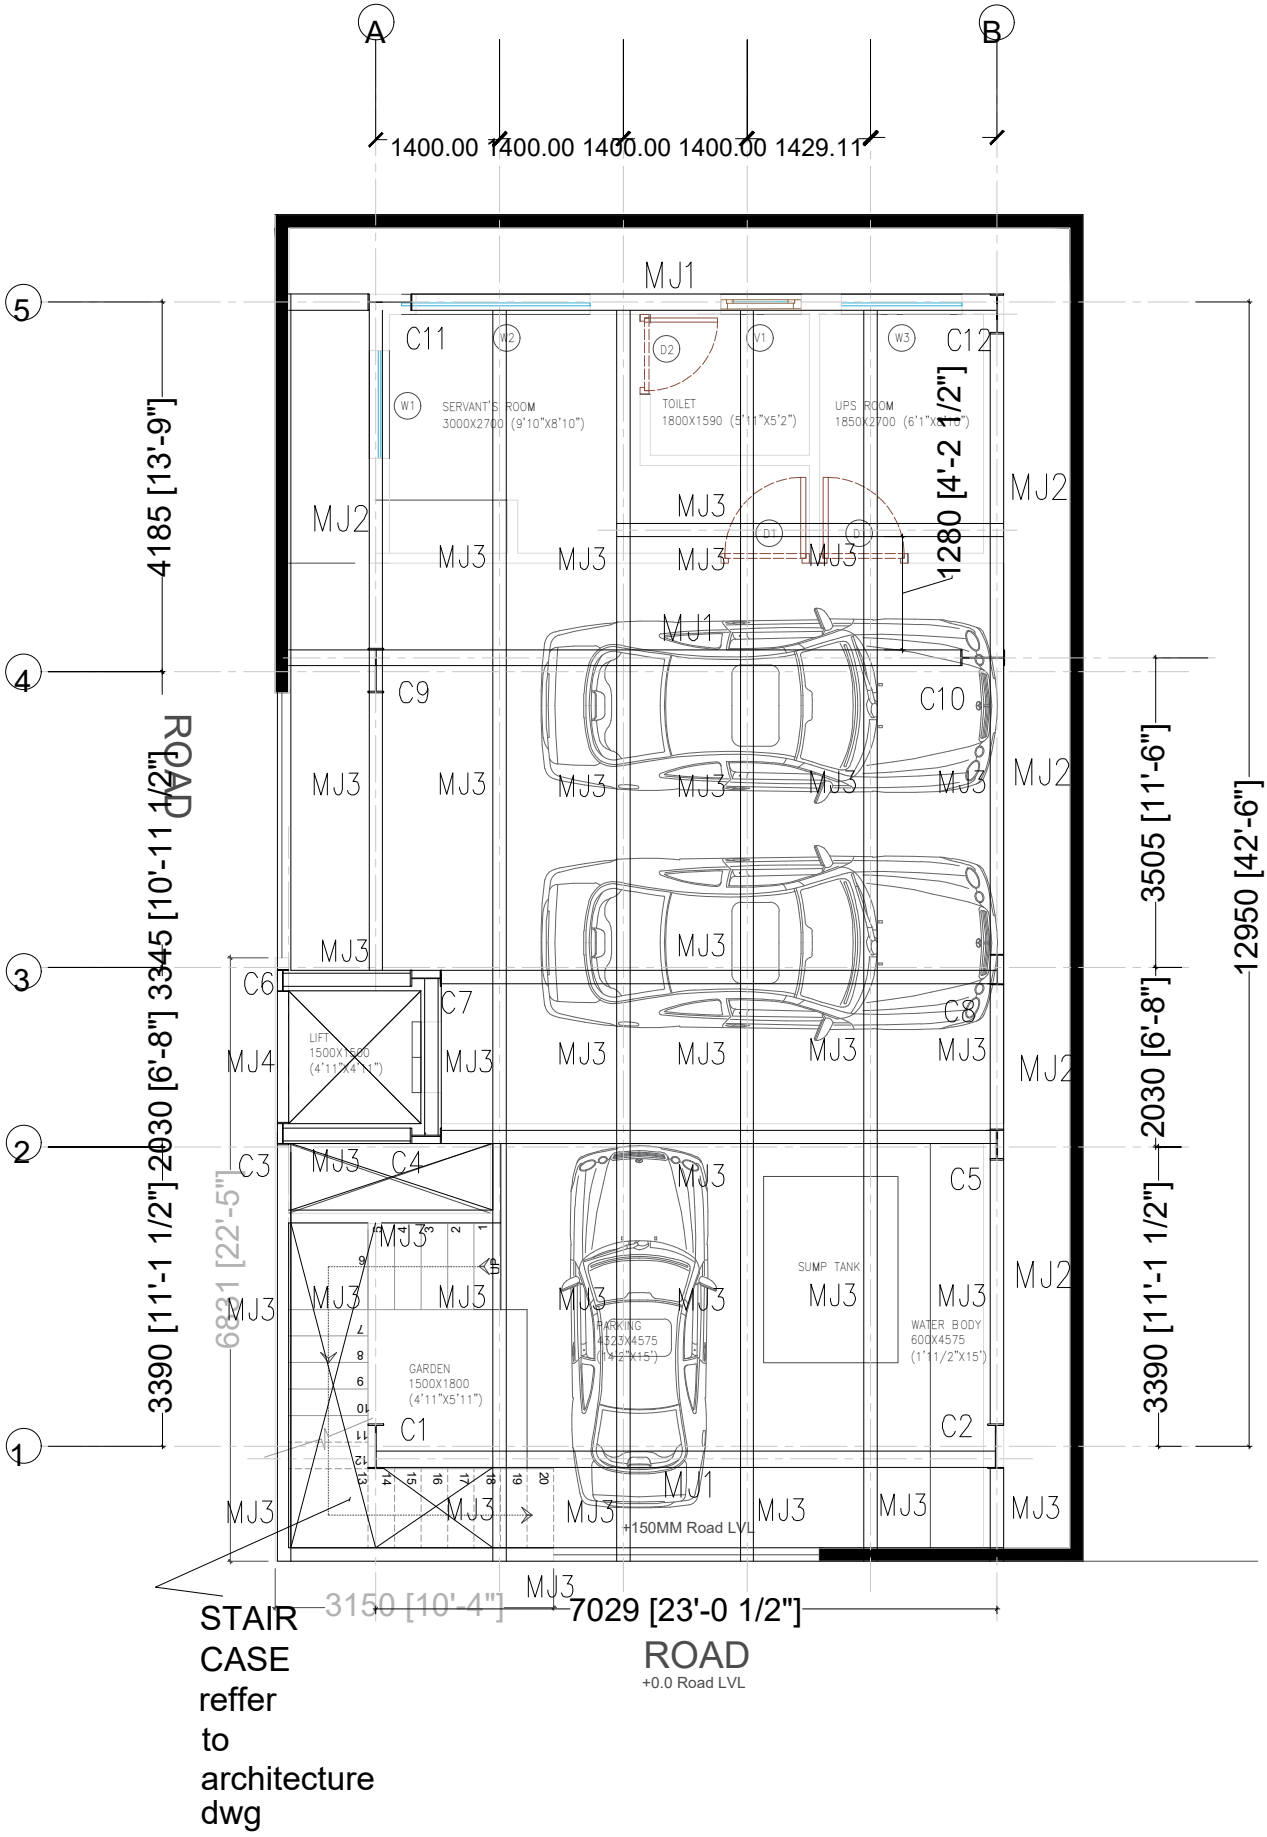

STAIR CASE reffer to architecture dwg

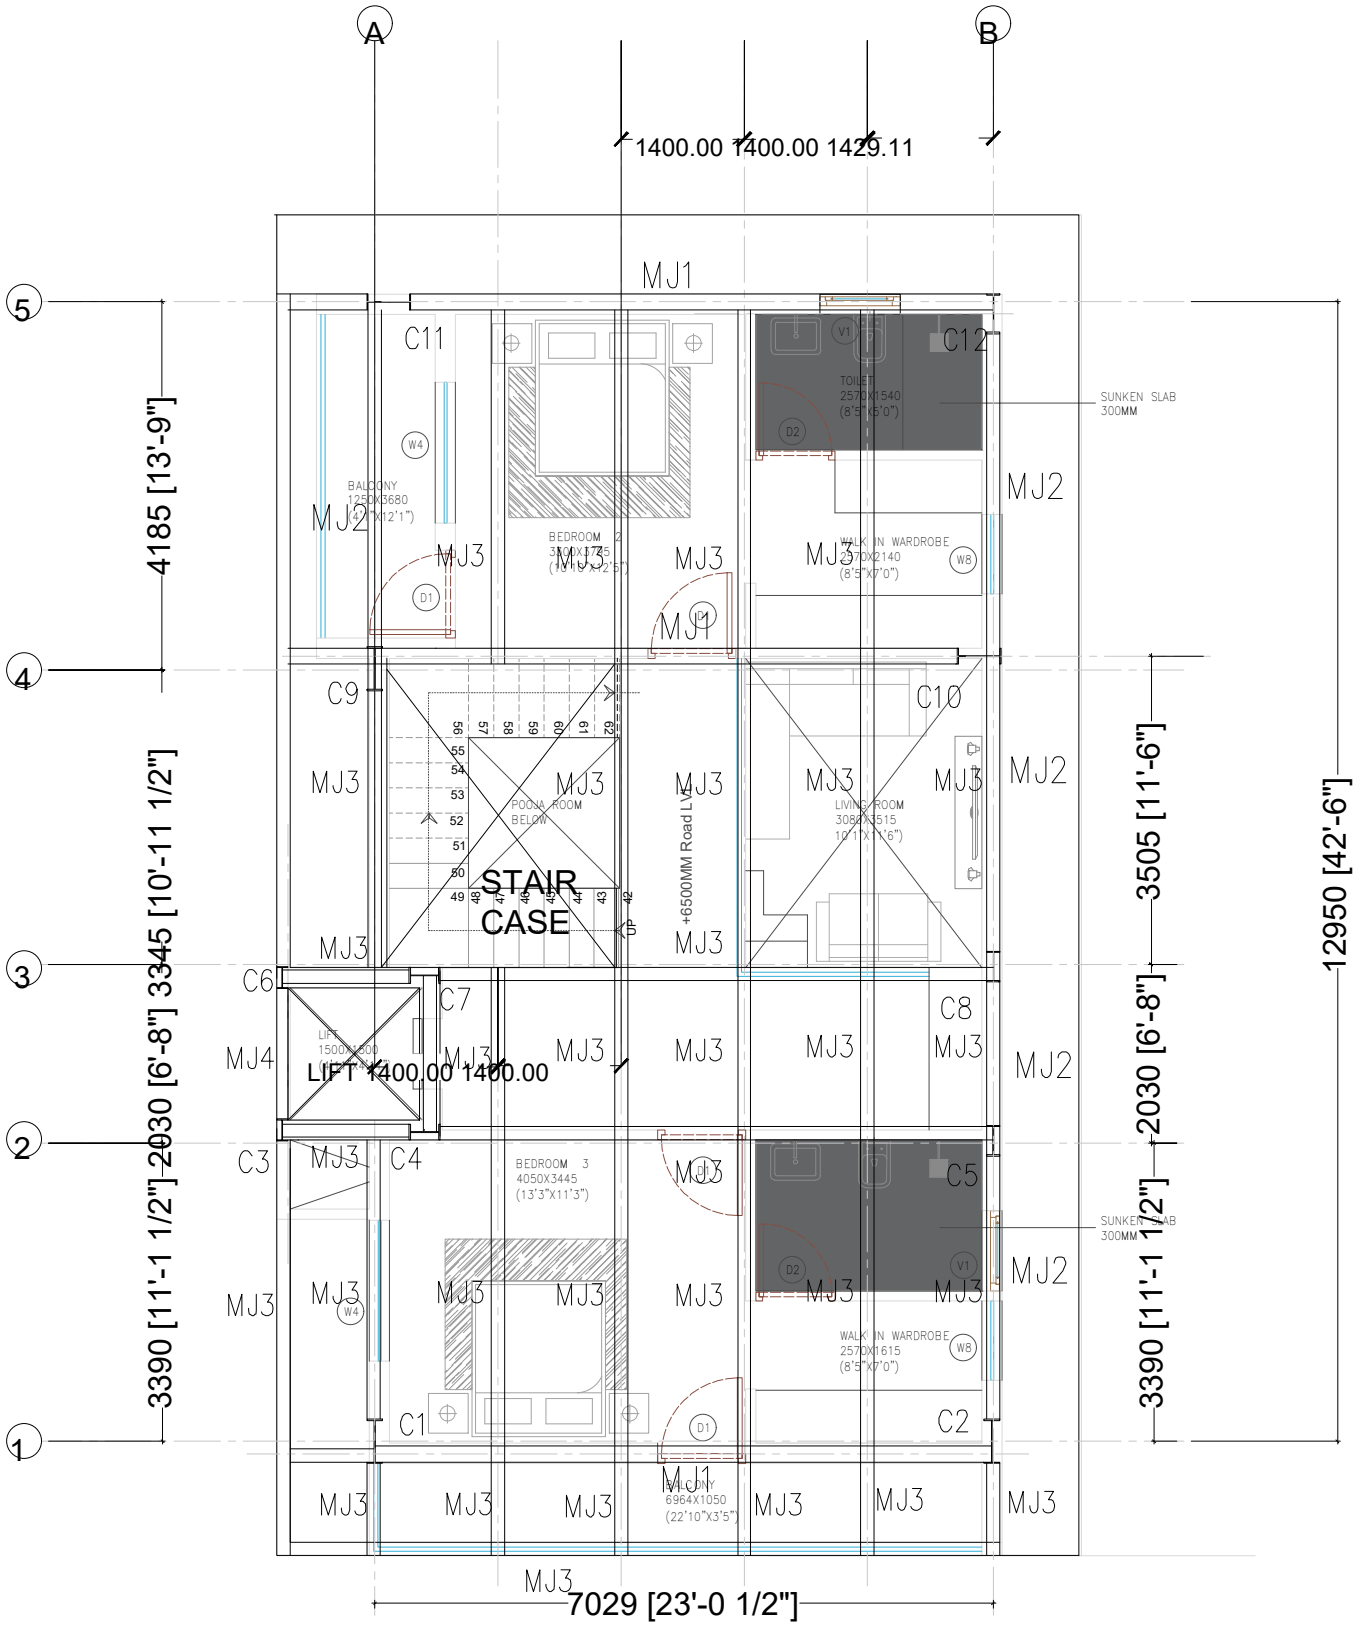
A
B
1400.00 1400.00 1429.11
MJ1
C11
C12
TOILET
2570X1540
(8'5"X5'0")
SUNKEN SLAB
300MM
BALCONY
1250X3680
(4'1"X12'1")
MJ2
BEDROOM 2
3300X3775
(10'10"X12'5")
WALK IN WARDROBE
2570X2140
(8'5"X7'0")
C9
C10
POOJA ROOM
BELOW
STAIR
CASE
+6500MM Road LVL
LIVING ROOM
3080X3515
(10'1"X11'6")
C6
C7
C8
LIFT
1500X1500
(4'11"X4'11")
MJ4
LIFT 1400.00 1400.00
C3
C4
BEDROOM 3
4050X3445
(13'3"X11'3")
C5
WALK IN WARDROBE
2570X1615
(8'5"X7'0")
C1
C2
BALCONY
6964X1050
(22'10"X3'5")
MJ3
7029 [23'-0 1/2"]
4185 [13'-9"]
3345 [10'-11 1/2"]
2030 [6'-8"]
3390 [11'-1 1/2"]
3505 [11'-6"]
2030 [6'-8"]
3390 [11'-1 1/2"]
12950 [42'-6"]